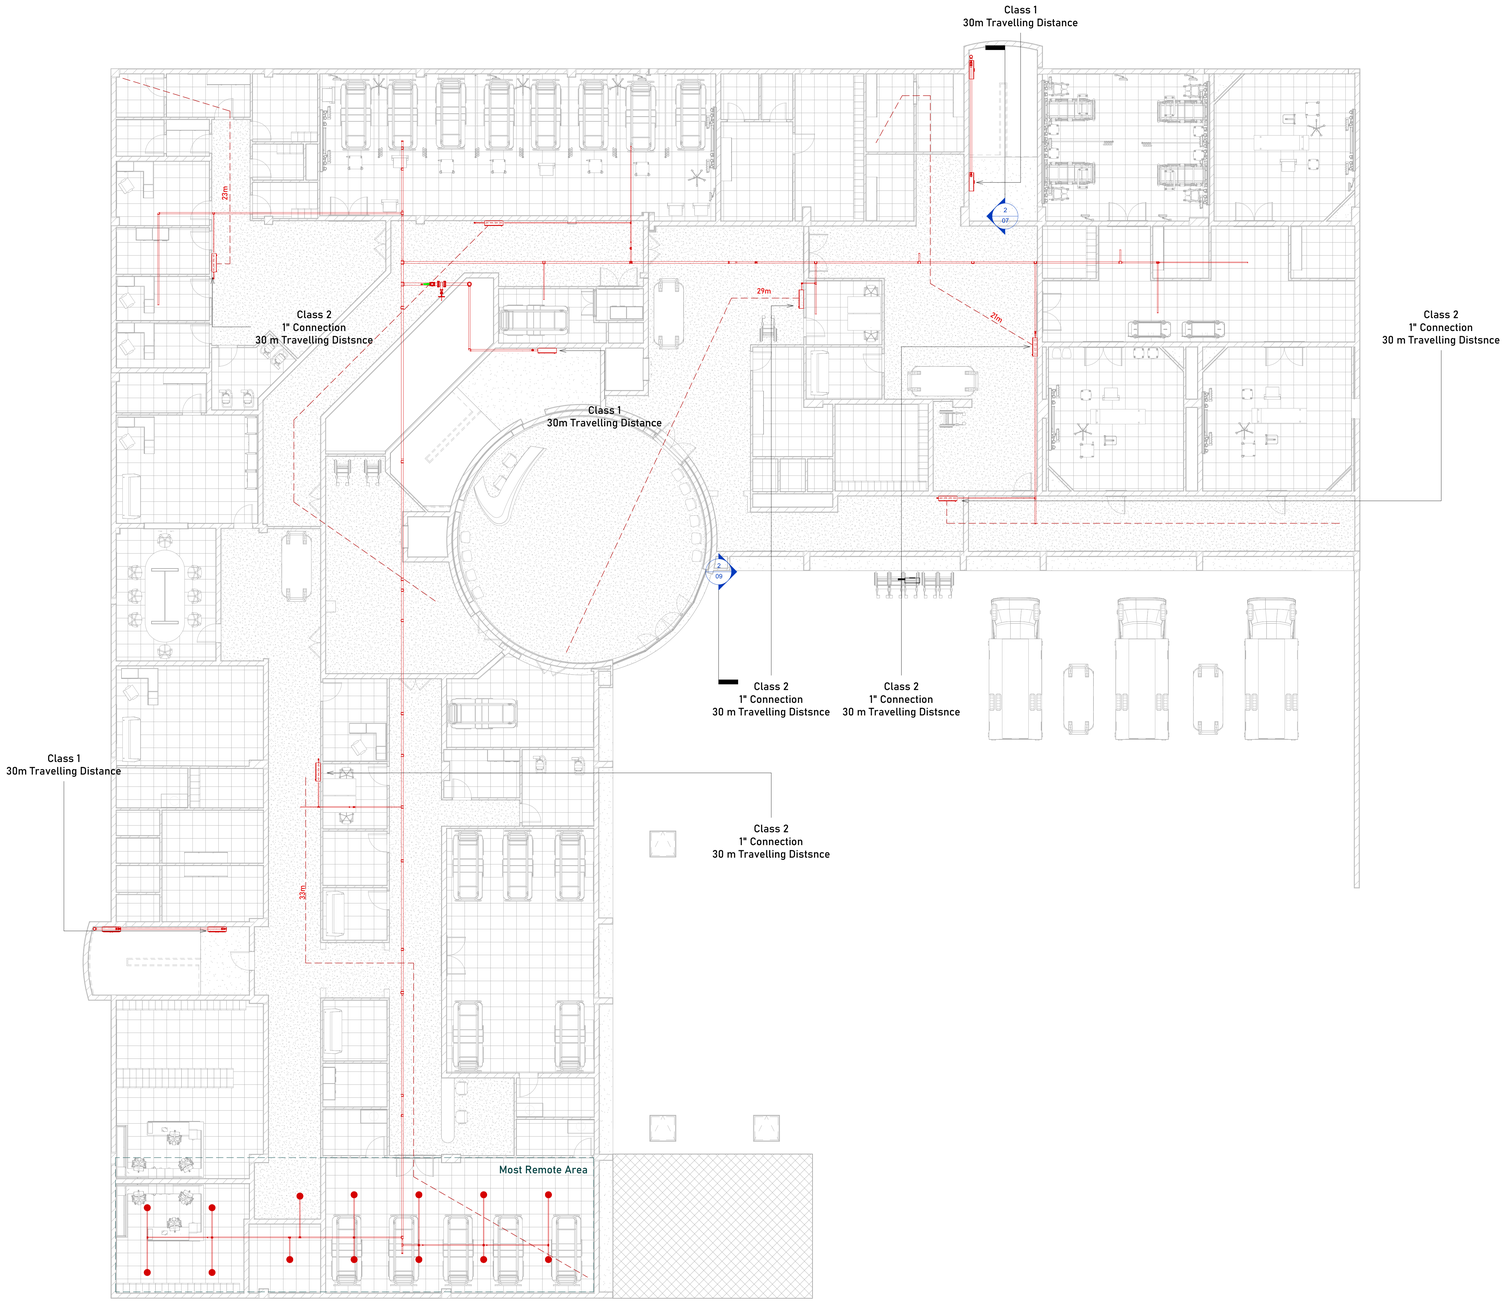

1 Hose Distribution
1 : 100

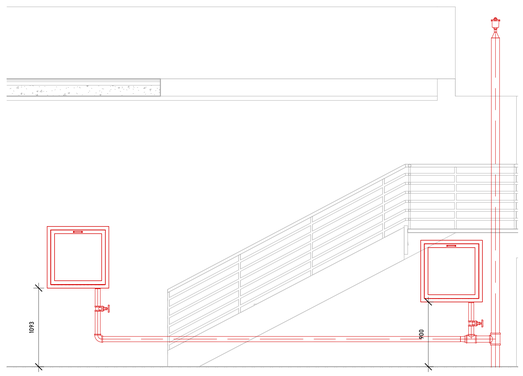

2 Stairs StandPipes
1 : 30

MOHAMED HADHOUD

KEY PLAN:

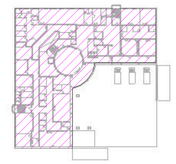

LEGEND:

	Upright Sprinkler		BASE HANGER
	PENDENT SPRINKLES		CHECK VALVE
	SIDEWALL SPRINKLES		PRESSURE GAUGE
	DIESEL PUMP		SUBMERSIBLE PUMP
	ELECTRIC PUMP		DIESEL TANK
	JOCKEY PUMP		FLOW METER
	CONCRETE FOUNDATION		FLOW SWITCH
	CONTROL PANEL		ALARM CHECK VALVE
	BATTERIES		BALL VALVE
	OS&Y VALVE		MUFFLER

Rev	Date	Detail	Made	Ch'd	App'd

constructor:
Engineer's Company for Electromechanical Works

Consultant :
ASEC For ElectroMechanical

Project :
Menofia Hospital

Title :
Ground Hose Distribution

Eng :	M.Hadhoud	CAD :	ENGX
Ch'd :	Hassan Salah	App'd :	ENGX
Date :	Issue Date	Scale :	As indicated

Drg. No. 07

Rev:

cm

A0