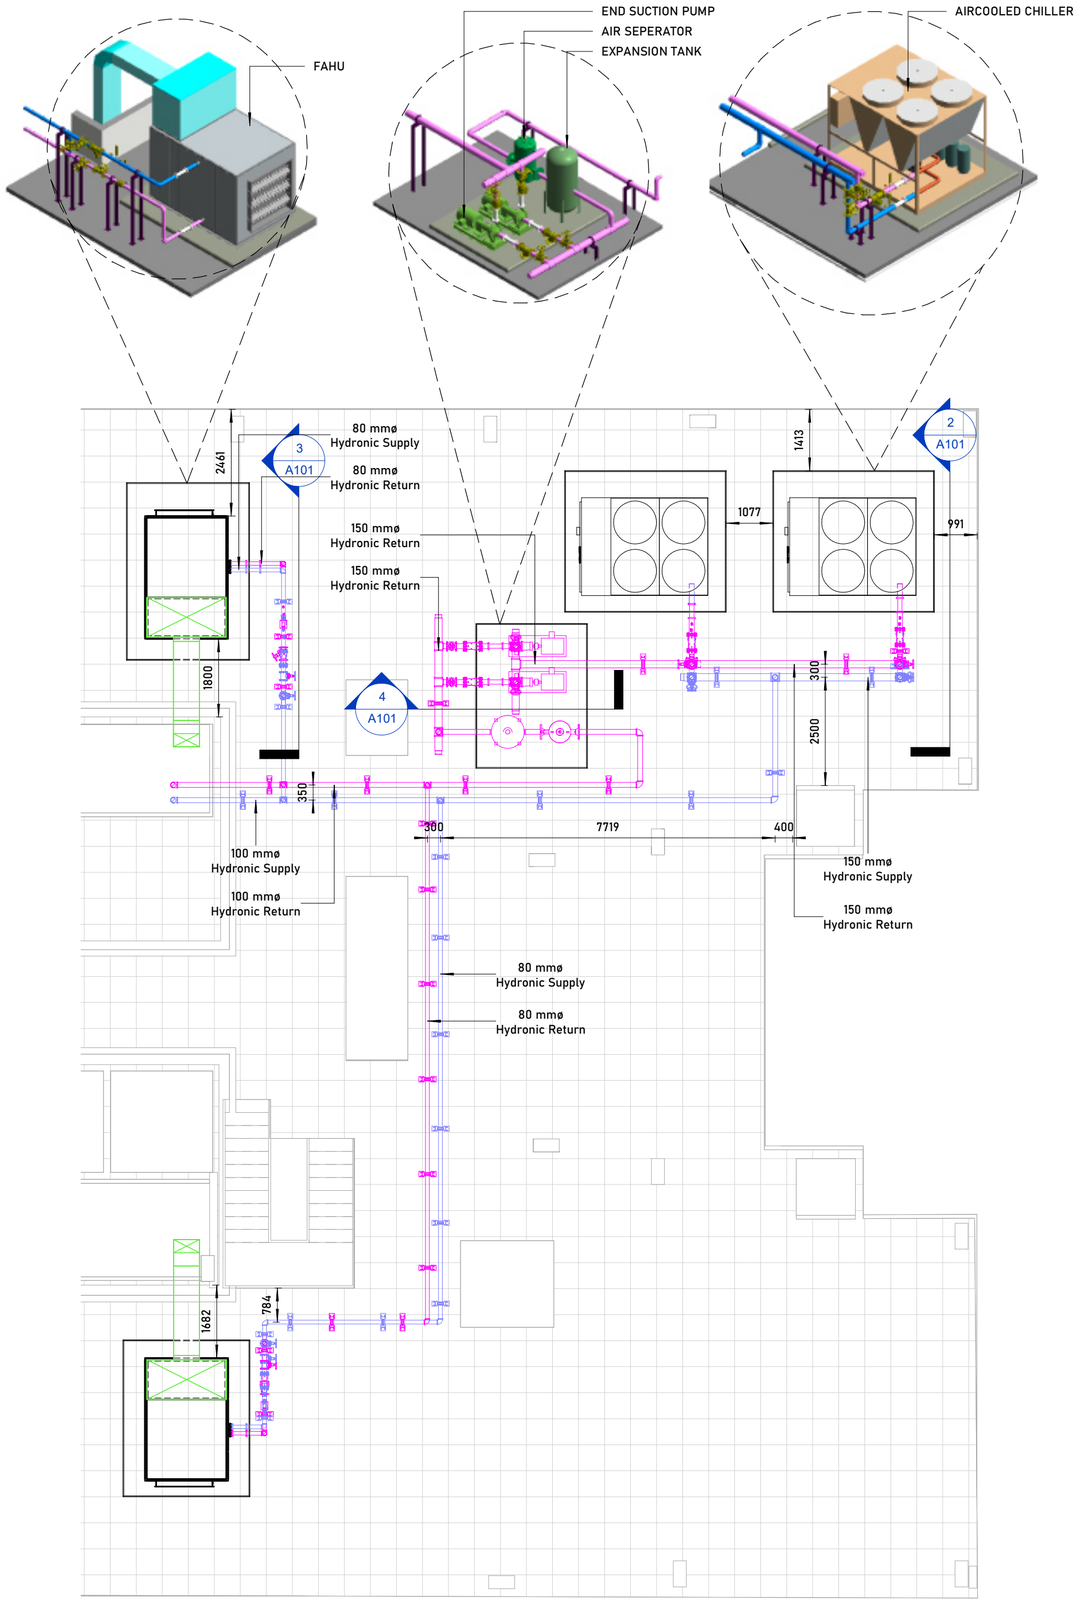

1 ROOF CHILLER PLANET

1 : 100

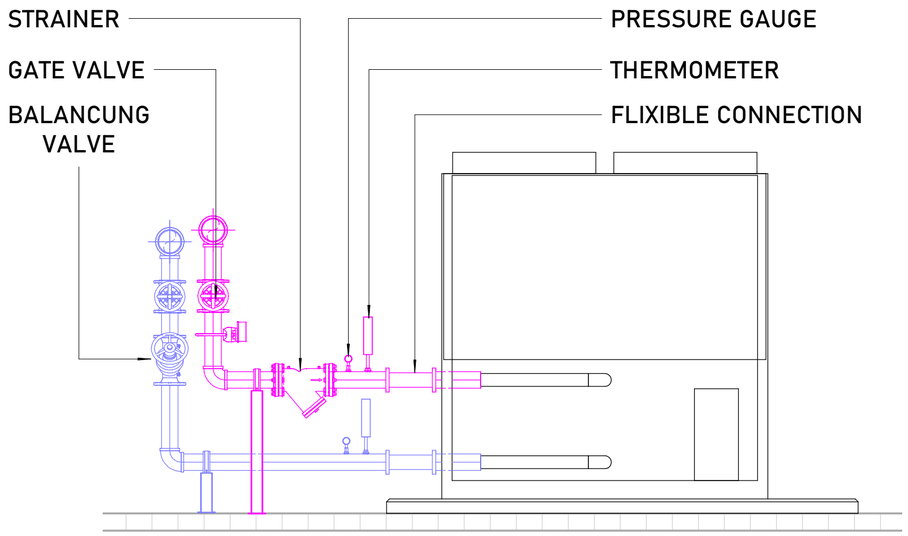

2 CHILLER HOOKUPS SECTION

1 : 30

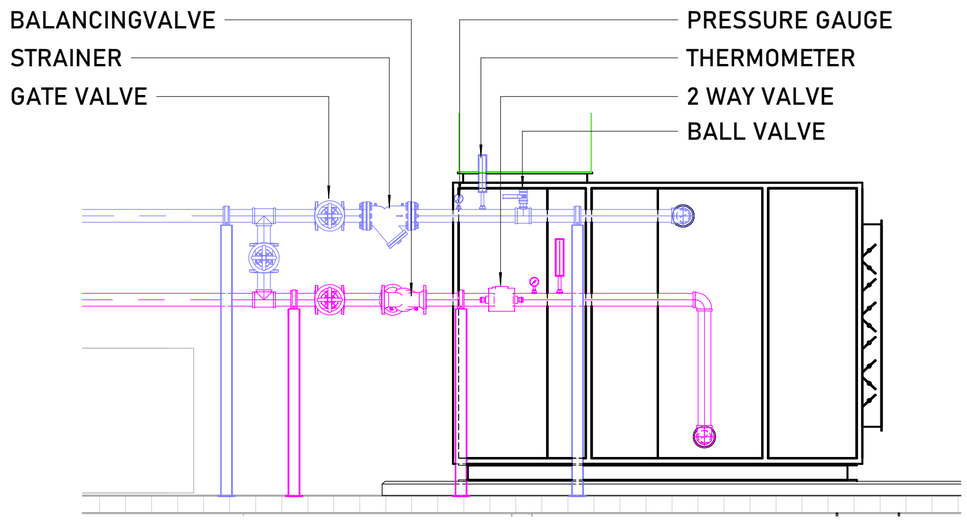

3 AHU HOOKUPS SECTION

1 : 30

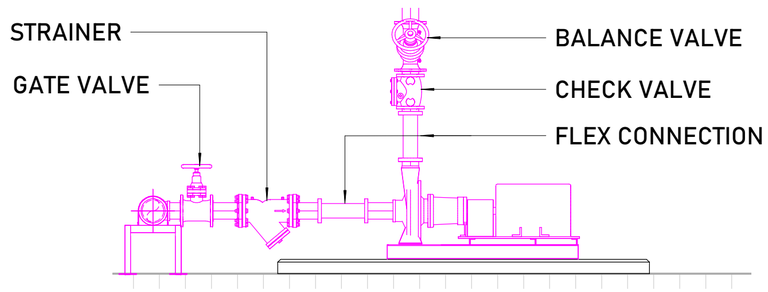

4 PUMP HOOKUPS SECTION

1 : 30

Key Plan

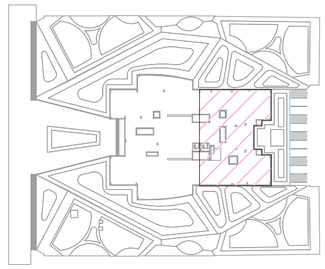

Notes:

1. DO NOT SCALE FROM THIS DRAWING.
2.ALL DIMENSIONS ARE IN mm, UNLESS OTHERWISE INDICATED

Legends:

SYMB	DISCRIBTION	SYMB	DISCRIBTION
	CONCRETE FOUND.		FLOOR HANGER
	CHILLER		SQUARE DIFFUSER
	FAN COIL UNIT		VOLUME DAMPER
	EXPANSION TANK		BALL VALVE
	END SUCTION PUMP		2 WAY VALVE
	FAHU		GATEVALVE
	STRAINER		SIDE WALL GRILL
	CHECK VALVE		SUPPLY AIR DUCT
	THERMOMETER		RETURN AIR DUCT
	AIR VENT		EXHAUST AIR DUCT
	BALANCIN VALVE		FRESH AIR DUCT
	AIR SEPARATOR		

Project:
SMART ARCH

Owner
:
https://linktr.ee/Eng_X
ENG.X ENGINEERING TRAINING

Date: 03/26/2025

Designer: ENG.M.A.HADHOUD

Checked by: H.ELMMOKABBATY

DRAWING:
ROOF FLOOR HVAC WORKS

DISCIPLINE: MECH-HVAC

Scale: AS DETECTED

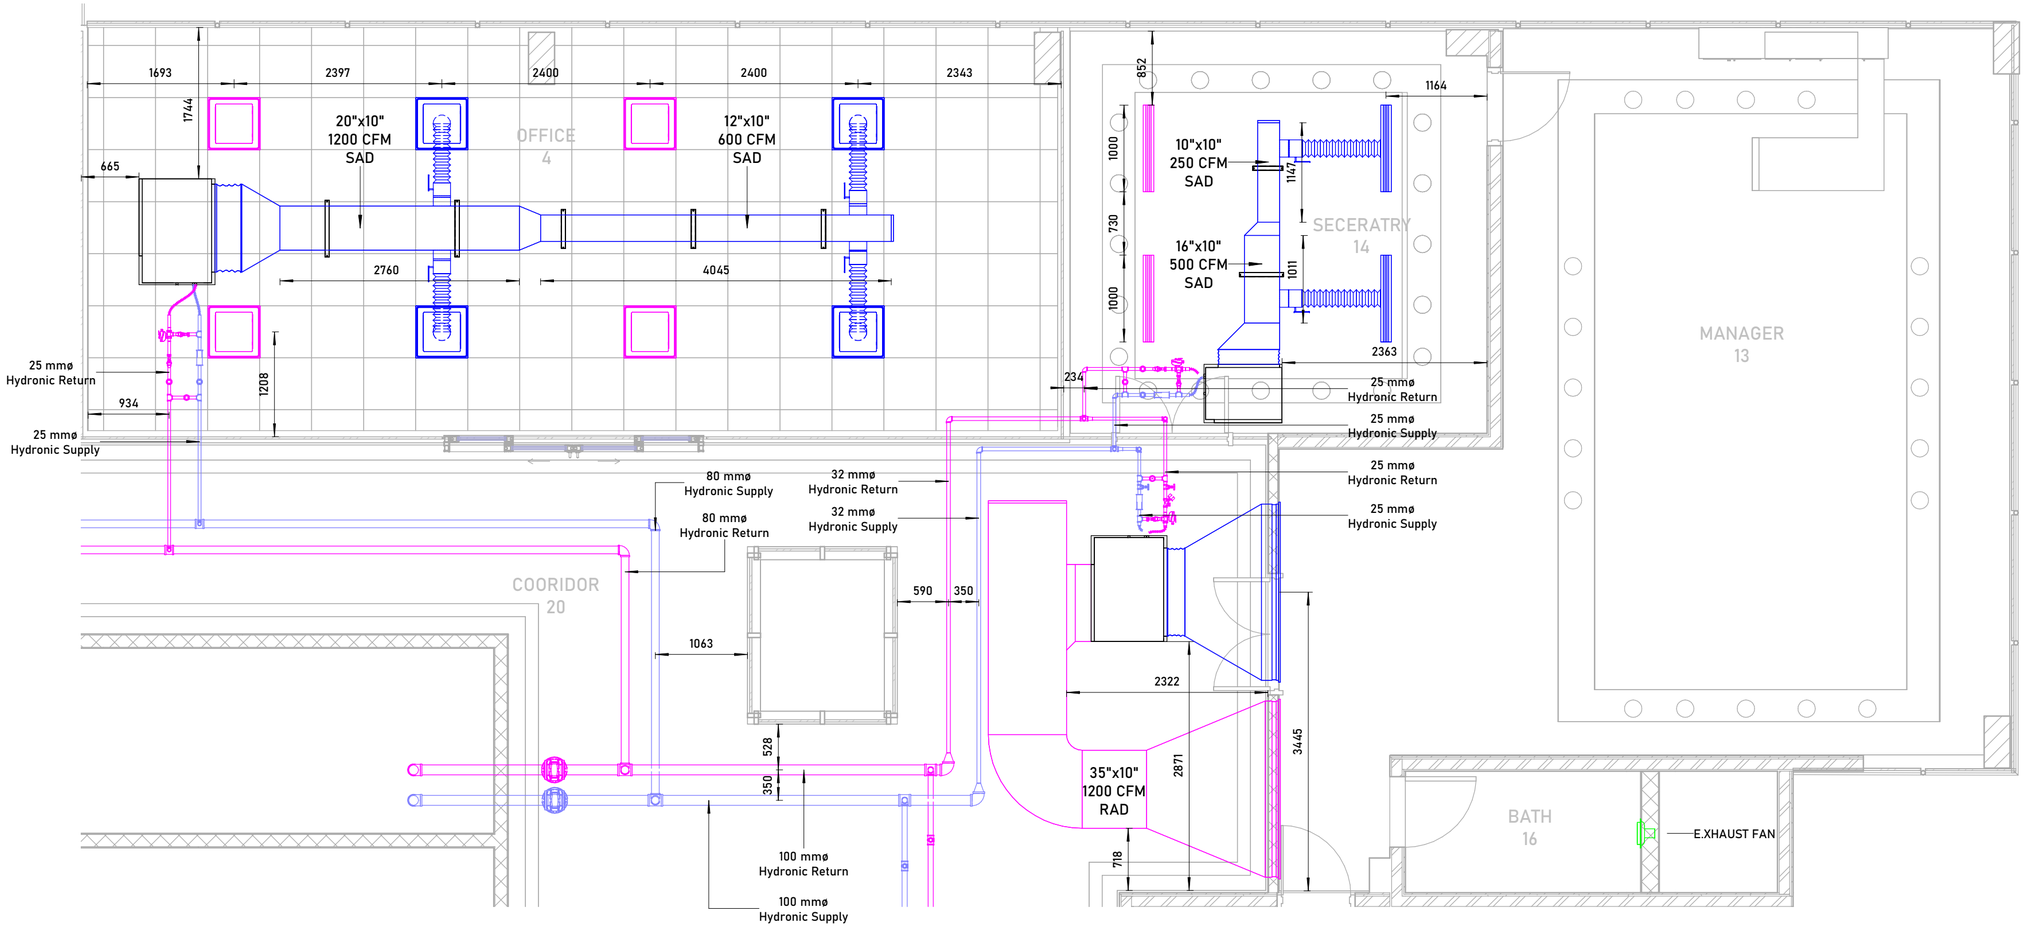

1 GROUND FLOOR task print

1 : 50

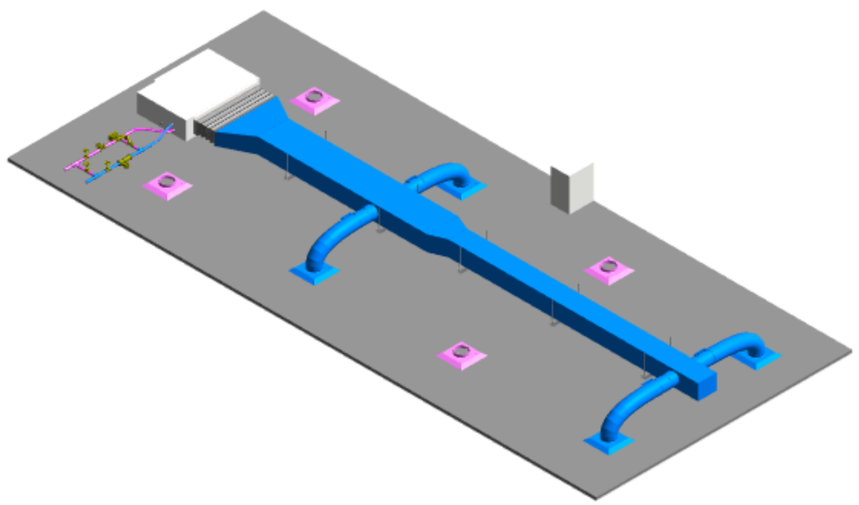

2 OFFICE 04

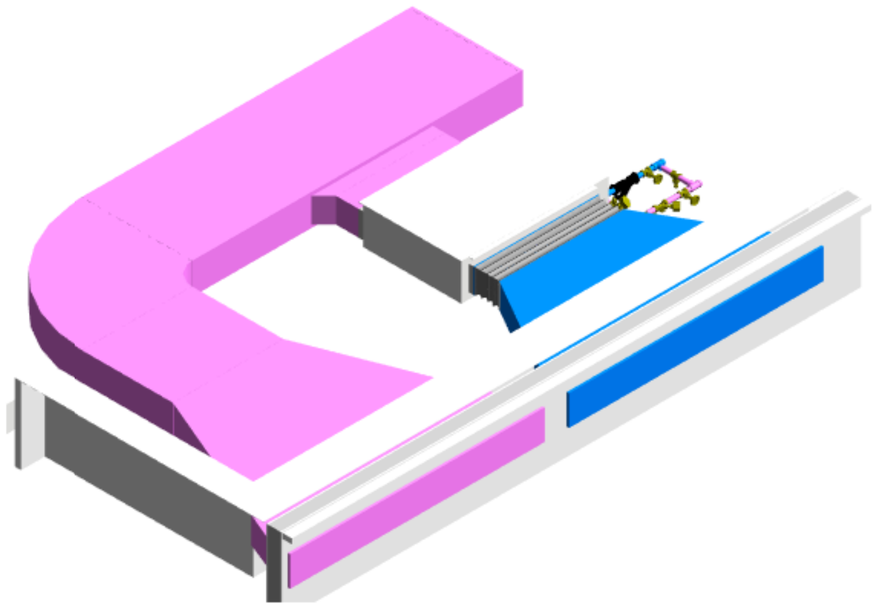

3 3D MANAGER HVAC WORK

Key Plan

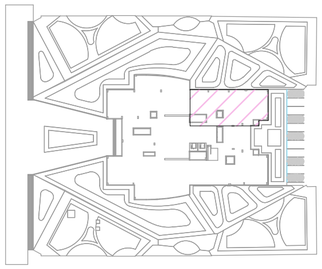

Notes:

1. DO NOT SCALE FROM THIS DRAWING.
2. ALL DIMENSIONS ARE IN mm, UNLESS OTHERWISE INDICATED

Legends:

SYMB	DISCRIBTION	SYMB	DISCRIBTION
	CONCRETE FOUND.		FLOOR HANGER
	CHILLER		SQUARE DIFFUSER
	FAN COIL UNIT		VOLUME DAMPER
	EXPANSION TANK		BALL VALVE
	END SUCTION PUMP		2 WAY VALVE
	FAHU		GATEVALVE
	STRAINER		SIDE WALL GRILL
	CHECK VALVE		SUPPLY AIR DUCT
	THERMOMETER		RETURN AIR DUCT
	AIR VENT		EXHAUST AIR DUCT
	BALANCIN VALVE		FRESH AIR DUCT
	AIR SEPARATOR		

Project:
SMART ARCH

Owner
:
https://linktr.ee/Eng_X
ENG.X ENGINEERING TRAINING

Date: 03/26/2025

Designer: ENG.M.A.HADHOUD

Checked by: H.ELMMOKABBATY

DRAWING:
GROUND FLOOR HVAC WORKS

DISCIPLINE: MECH-HVAC

Scale: AS DETECTED

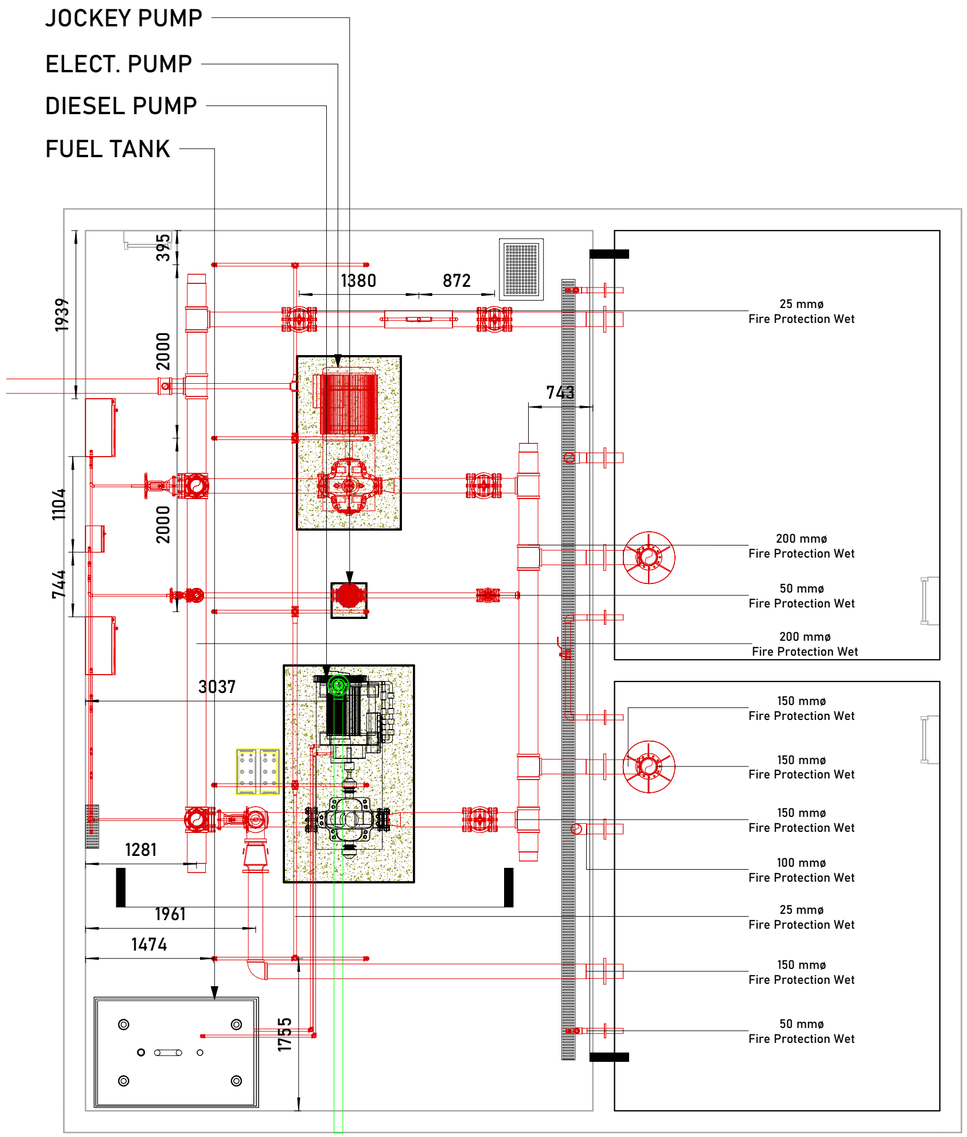

1 FIRE FIGHTINING PYUMP ROOM

1 : 50

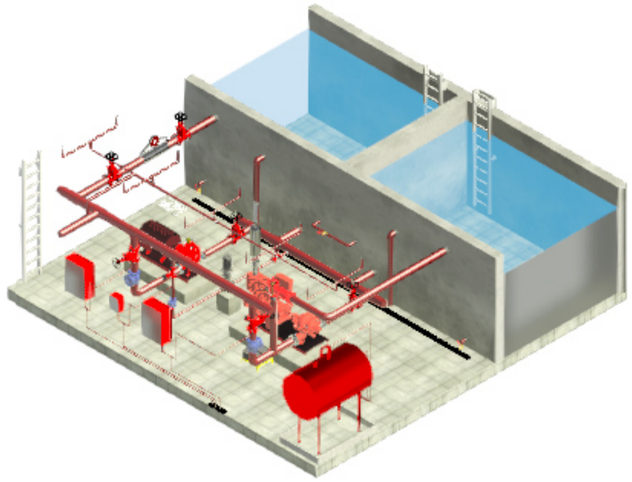

4 3D PUMP ROOM

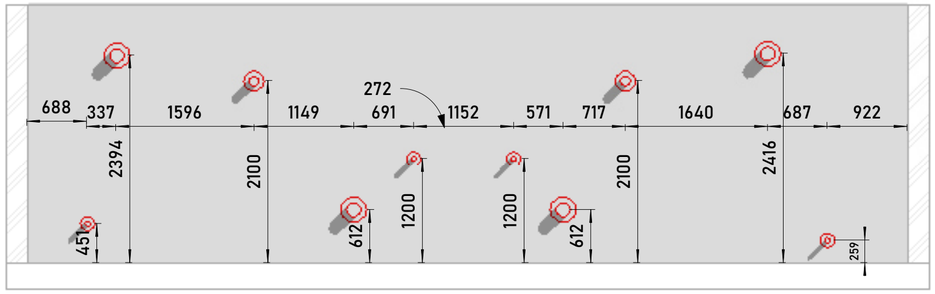

2 TANK PIPES

1 : 50

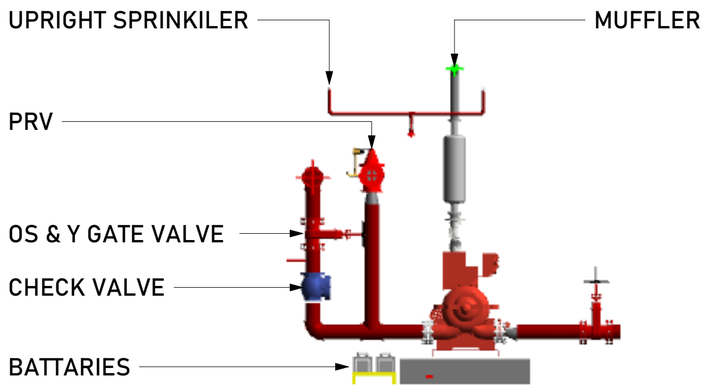

3 DIESEL PUMP HOOKUPS

1 : 50

Key Plan

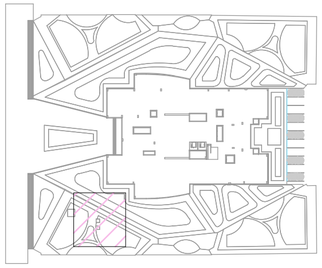

Notes:

1. DO NOT SCALE FROM THIS DRAWING.
2.ALL DIMENSIONS ARE IN mm, UNLESS OTHERWISE INDICATED

Legends:

	UPRIGHT SPRINKLERS		BASE HANGER
	PENDENT SPRINKLES		CHECK VALVE
	SIDEWALL SPRINKLES		PRESSURE GAUGE
	DIESEL PUMP		SUBMERSIBLE PUMP
	ELECTRIC PUMP		DIESEL TANK
	JOCKEY PUMP		FLOW METER
	CONCRETE FOUNDATION		FLOW SWITCH
	CONTROL PANEL		ALARM CHECK VALVE
	BATTERIES		BALL VALVE
	OS&Y VALVE		MUFFLER

Project:
SMART OFFICE

Owner
:
https://linktr.ee/Eng_X
ENG.X ENGINEERING TRAINING

Date: 04/10/2025

Designer: ENG.M.A.HADHOUD

Checked by: H.ELMOKABBATY

DRAWING:
FIREFIGHTING PUMP ROOM

DISCIPLINE: FIREFIGHTING

Scale: AS DETECTED

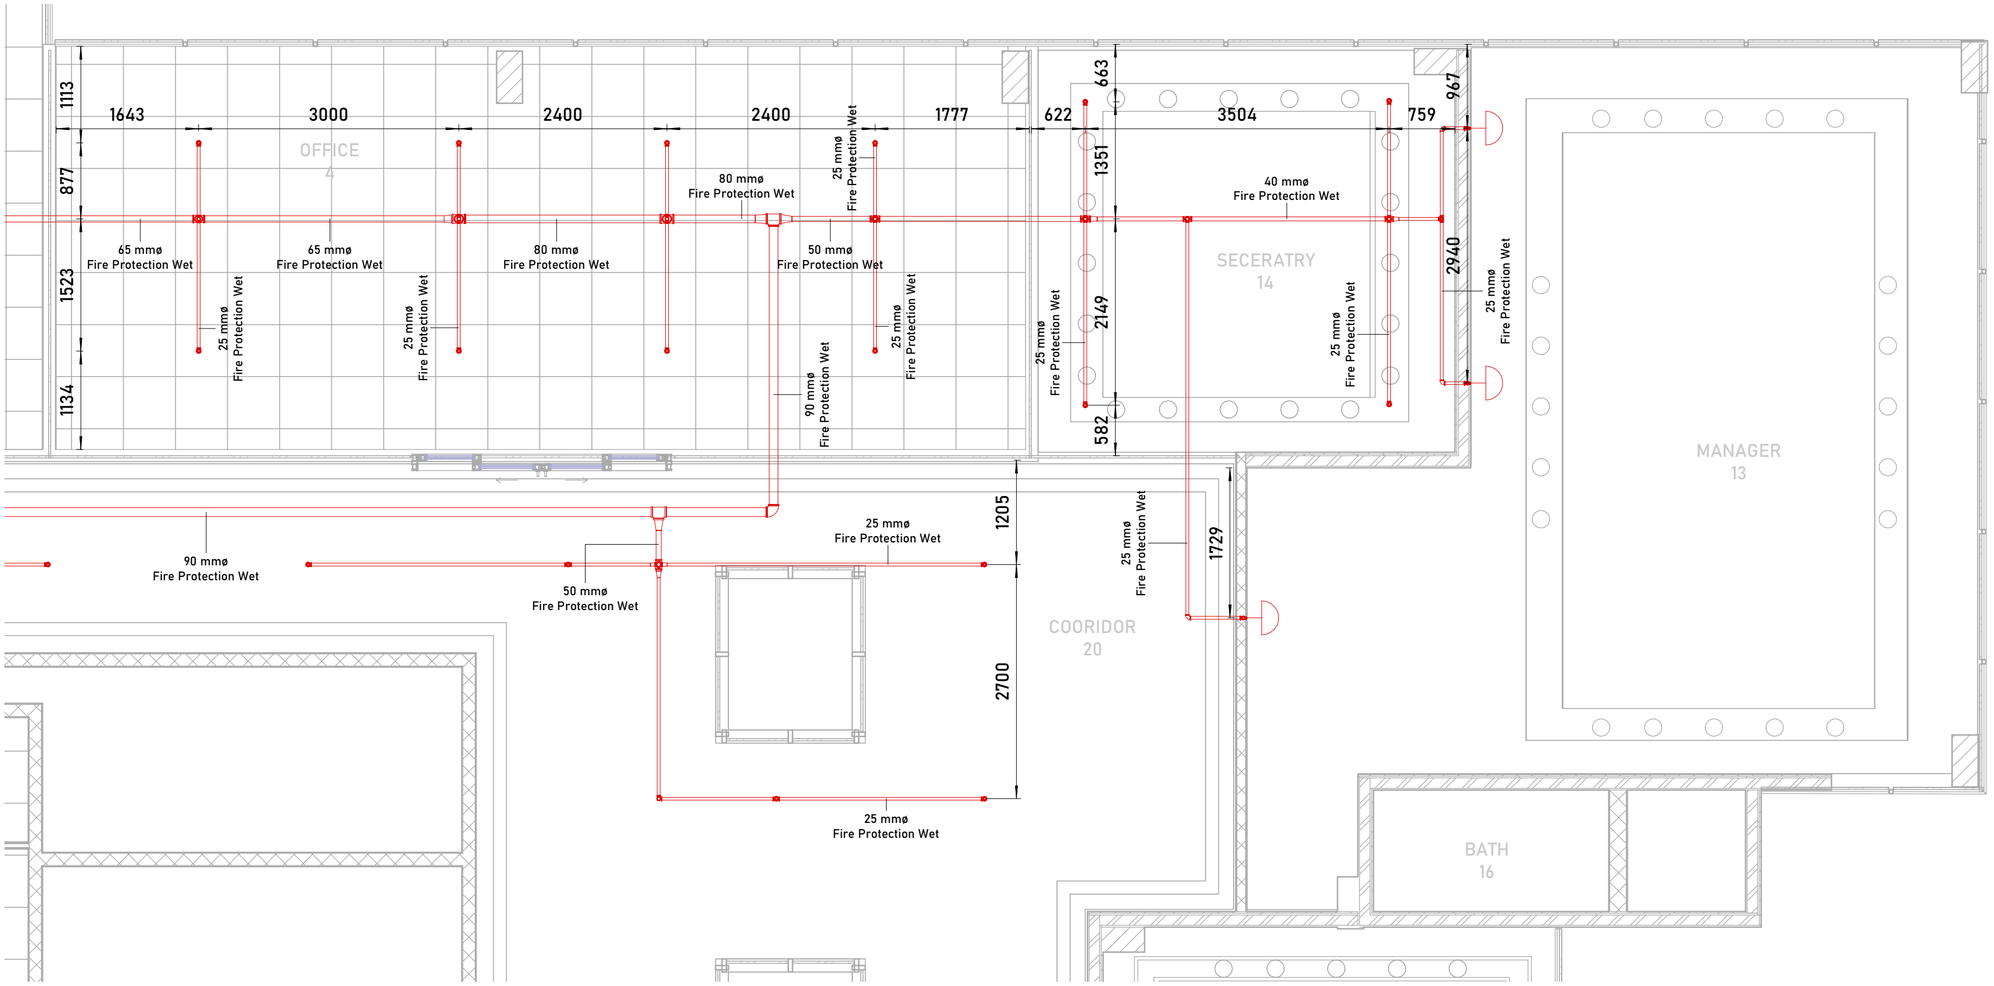

1 GROUND FLOOR task print

1 : 50

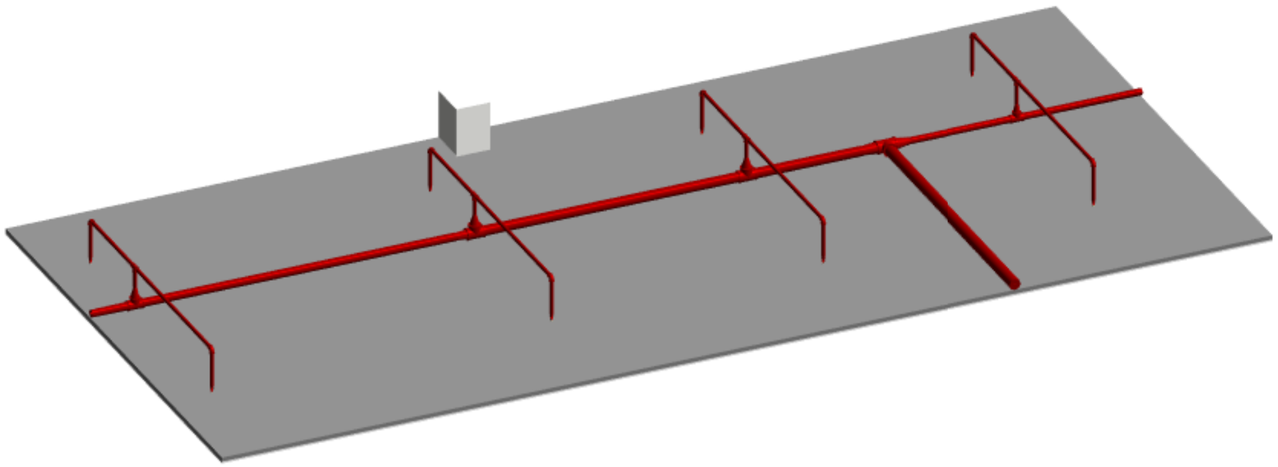

2 OFFICE SPRINKILERS DISTRIBUTION

Key Plan

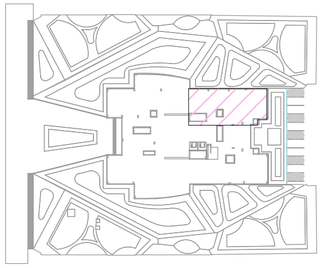

Notes:

1. DO NOT SCALE FROM THIS DRAWING.
2. ALL DIMENSIONS ARE IN mm, UNLESS OTHERWISE INDICATED

Legends:

	UPRIGHT SPRINKLERS		BASE HANGER
	PENDENT SPRINKLES		CHECK VALVE
	SIDEWALL SPRINKLES		PRESSURE GAUGE
	DIESEL PUMP		SUBMERSIBLE PUMP
	ELECTRIC PUMP		DIESEL TANK
	JOCKEY PUMP		FLOW METER
	CONCRETE FOUNDATION		FLOW SWITCH
	CONTROL PANEL		ALARM CHECK VALVE
	BATTERIES		BALL VALVE
	OS&Y VALVE		MUFFLER

Project:
SMART OFFICE

Owner
:
:
https://linktr.ee/Eng_X
ENG.X ENGINEERING TRAINING

Date: 04/10/2025

Designer: ENG.M.A.HADHOUD

Checked by: H.ELMOKABBATY

DRAWING:
SPACES SPRINKILER DIST.

DISCIPLINE: FIREFIGHTING

Scale: AS DETECTED

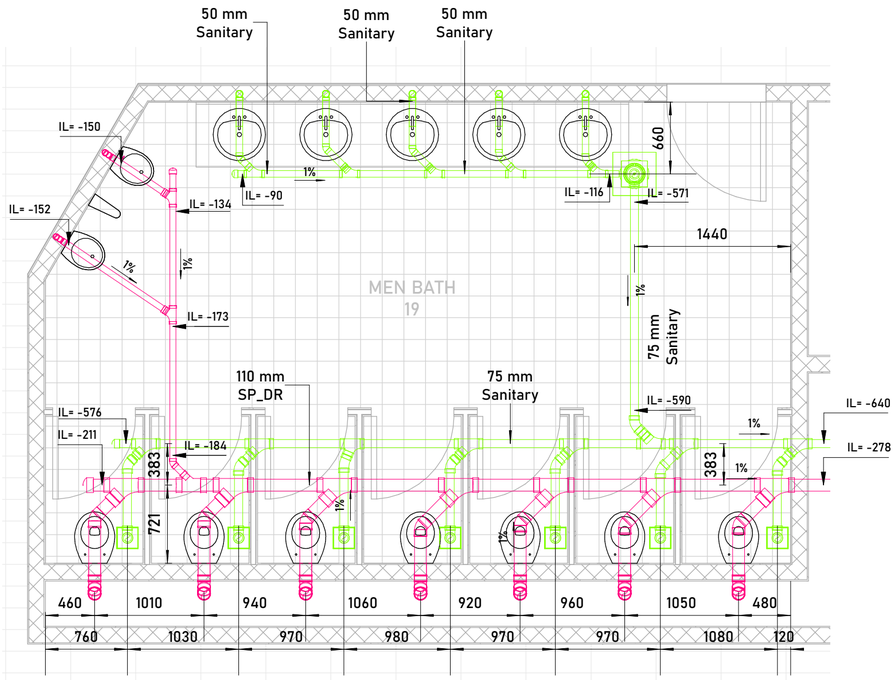

1 BATHROOM DRAIN SYSTEM

1 : 40

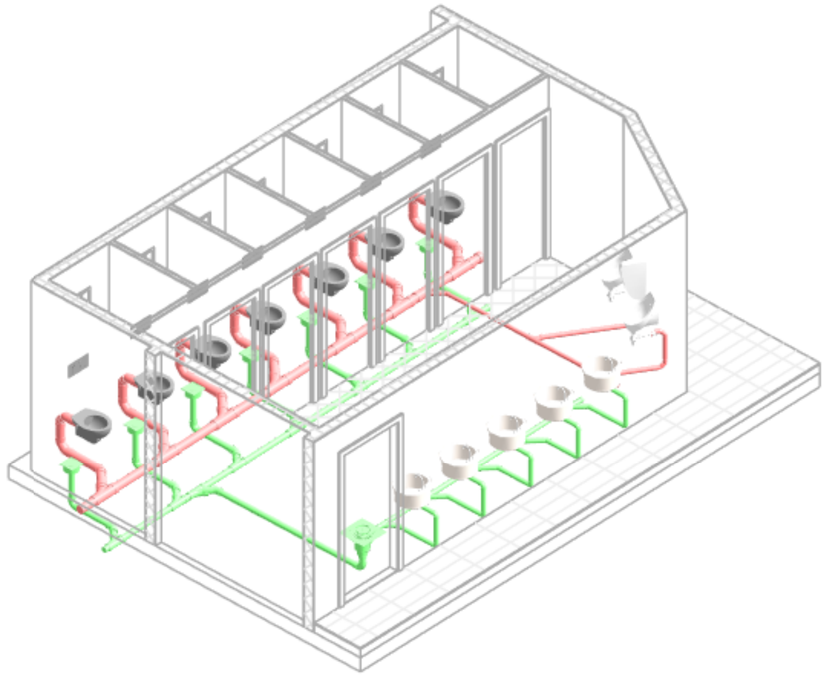

2 3D PATHROOM

Key Plan

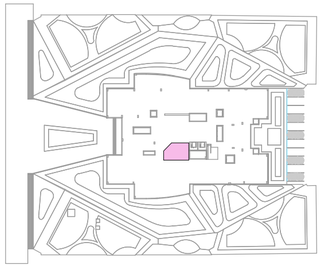

Notes:

1. DO NOT SCALE FROM THIS DRAWING.
2.ALL DIMENSIONS ARE IN mm, UNLESS OTHERWISE INDICATED

Legends:

	FLOOR DRAIN		ANGEL VALVE
	ELECTRIC HEATER		GATE VALVE

Project:
SMART OFFICE

Owner
:
:
https://linktr.ee/Eng_X
ENG.X ENGINEERING TRAINING

Date: 04/10/2025

Designer: ENG.M.A.HADHOUD

Checked by: H.ELMOKABBATY

DRAWING:
DRAIN SYSTEM

DISCIPLINE: PLUMPING

Scale: AS DETECTED

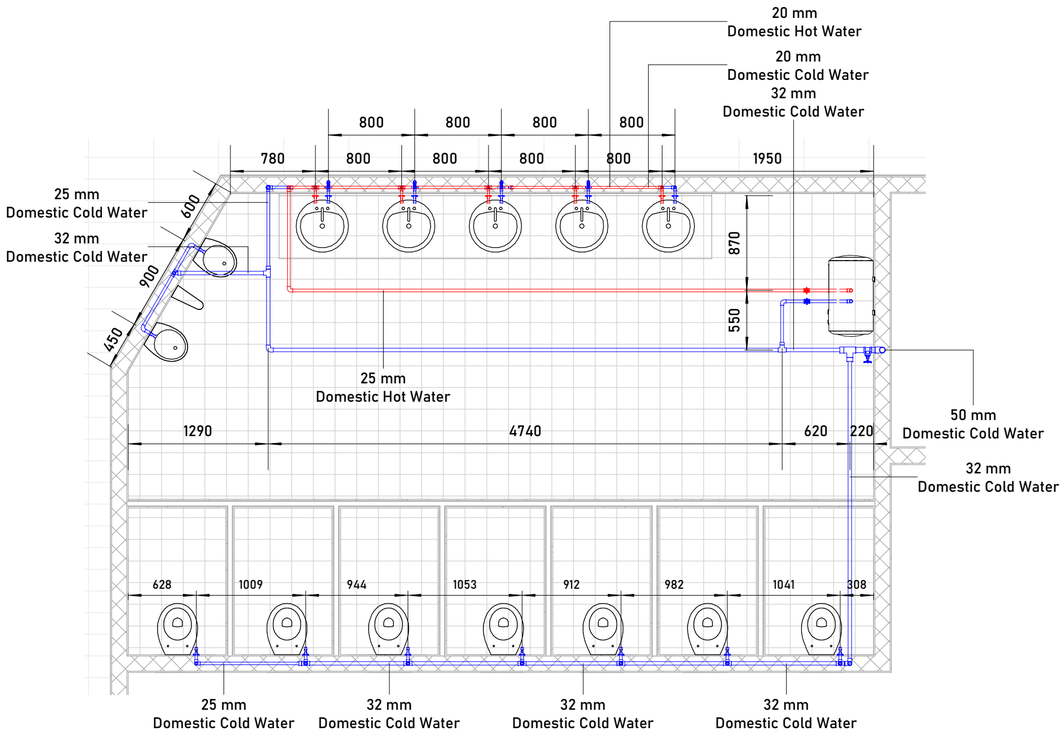

1 BATHROOM DOMESTIC SYSTEM

1 : 40

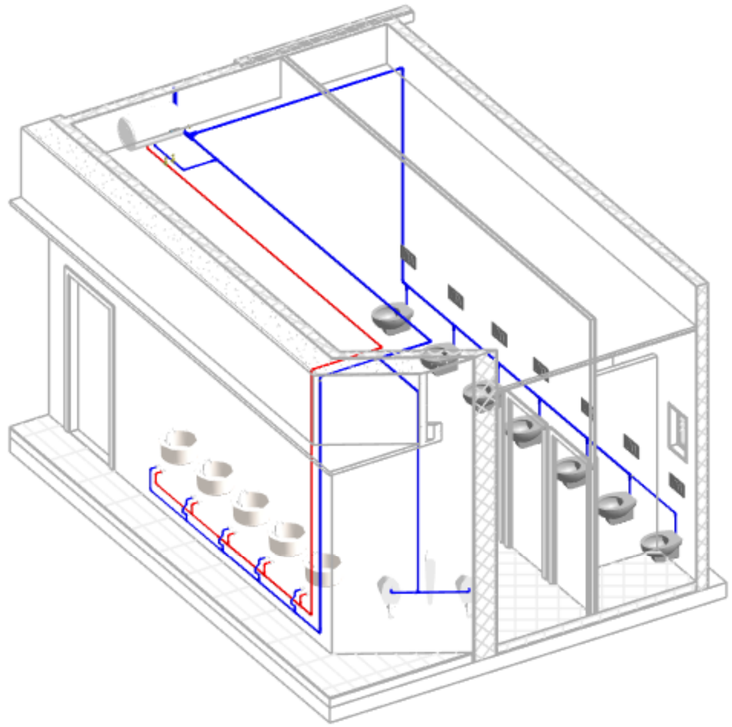

2 3D DOMESTIC BATHROOM

Key Plan

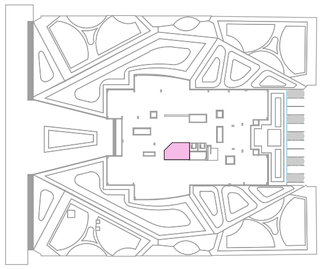

Notes:

1. DO NOT SCALE FROM THIS DRAWING.
2.ALL DIMENSIONS ARE IN mm, UNLESS OTHERWISE INDICATED

Legends:

	FLOOR DRAIN		ANGEL VALVE
	ELECTRIC HEATER		GATE VALVE

Project:
SMART OFFICE

Owner
:
https://linktr.ee/Eng_X
ENG.X ENGINEERING TRAINING

Date: 04/10/2025

Designer: ENG.M.A.HADHOUD

Checked by: H.ELMOKABBATY

DRAWING:
DOMESTIC SUPPLY SYSTEM

DISCIPLINE: PLUMBIING

Scale: AS DETECTED